


VUE DE FACE

Échelle 1:10 - jeu 2 mm entre portes et avec les habillages - sol plus bas de ~1 cm à droite (à l'échelle)

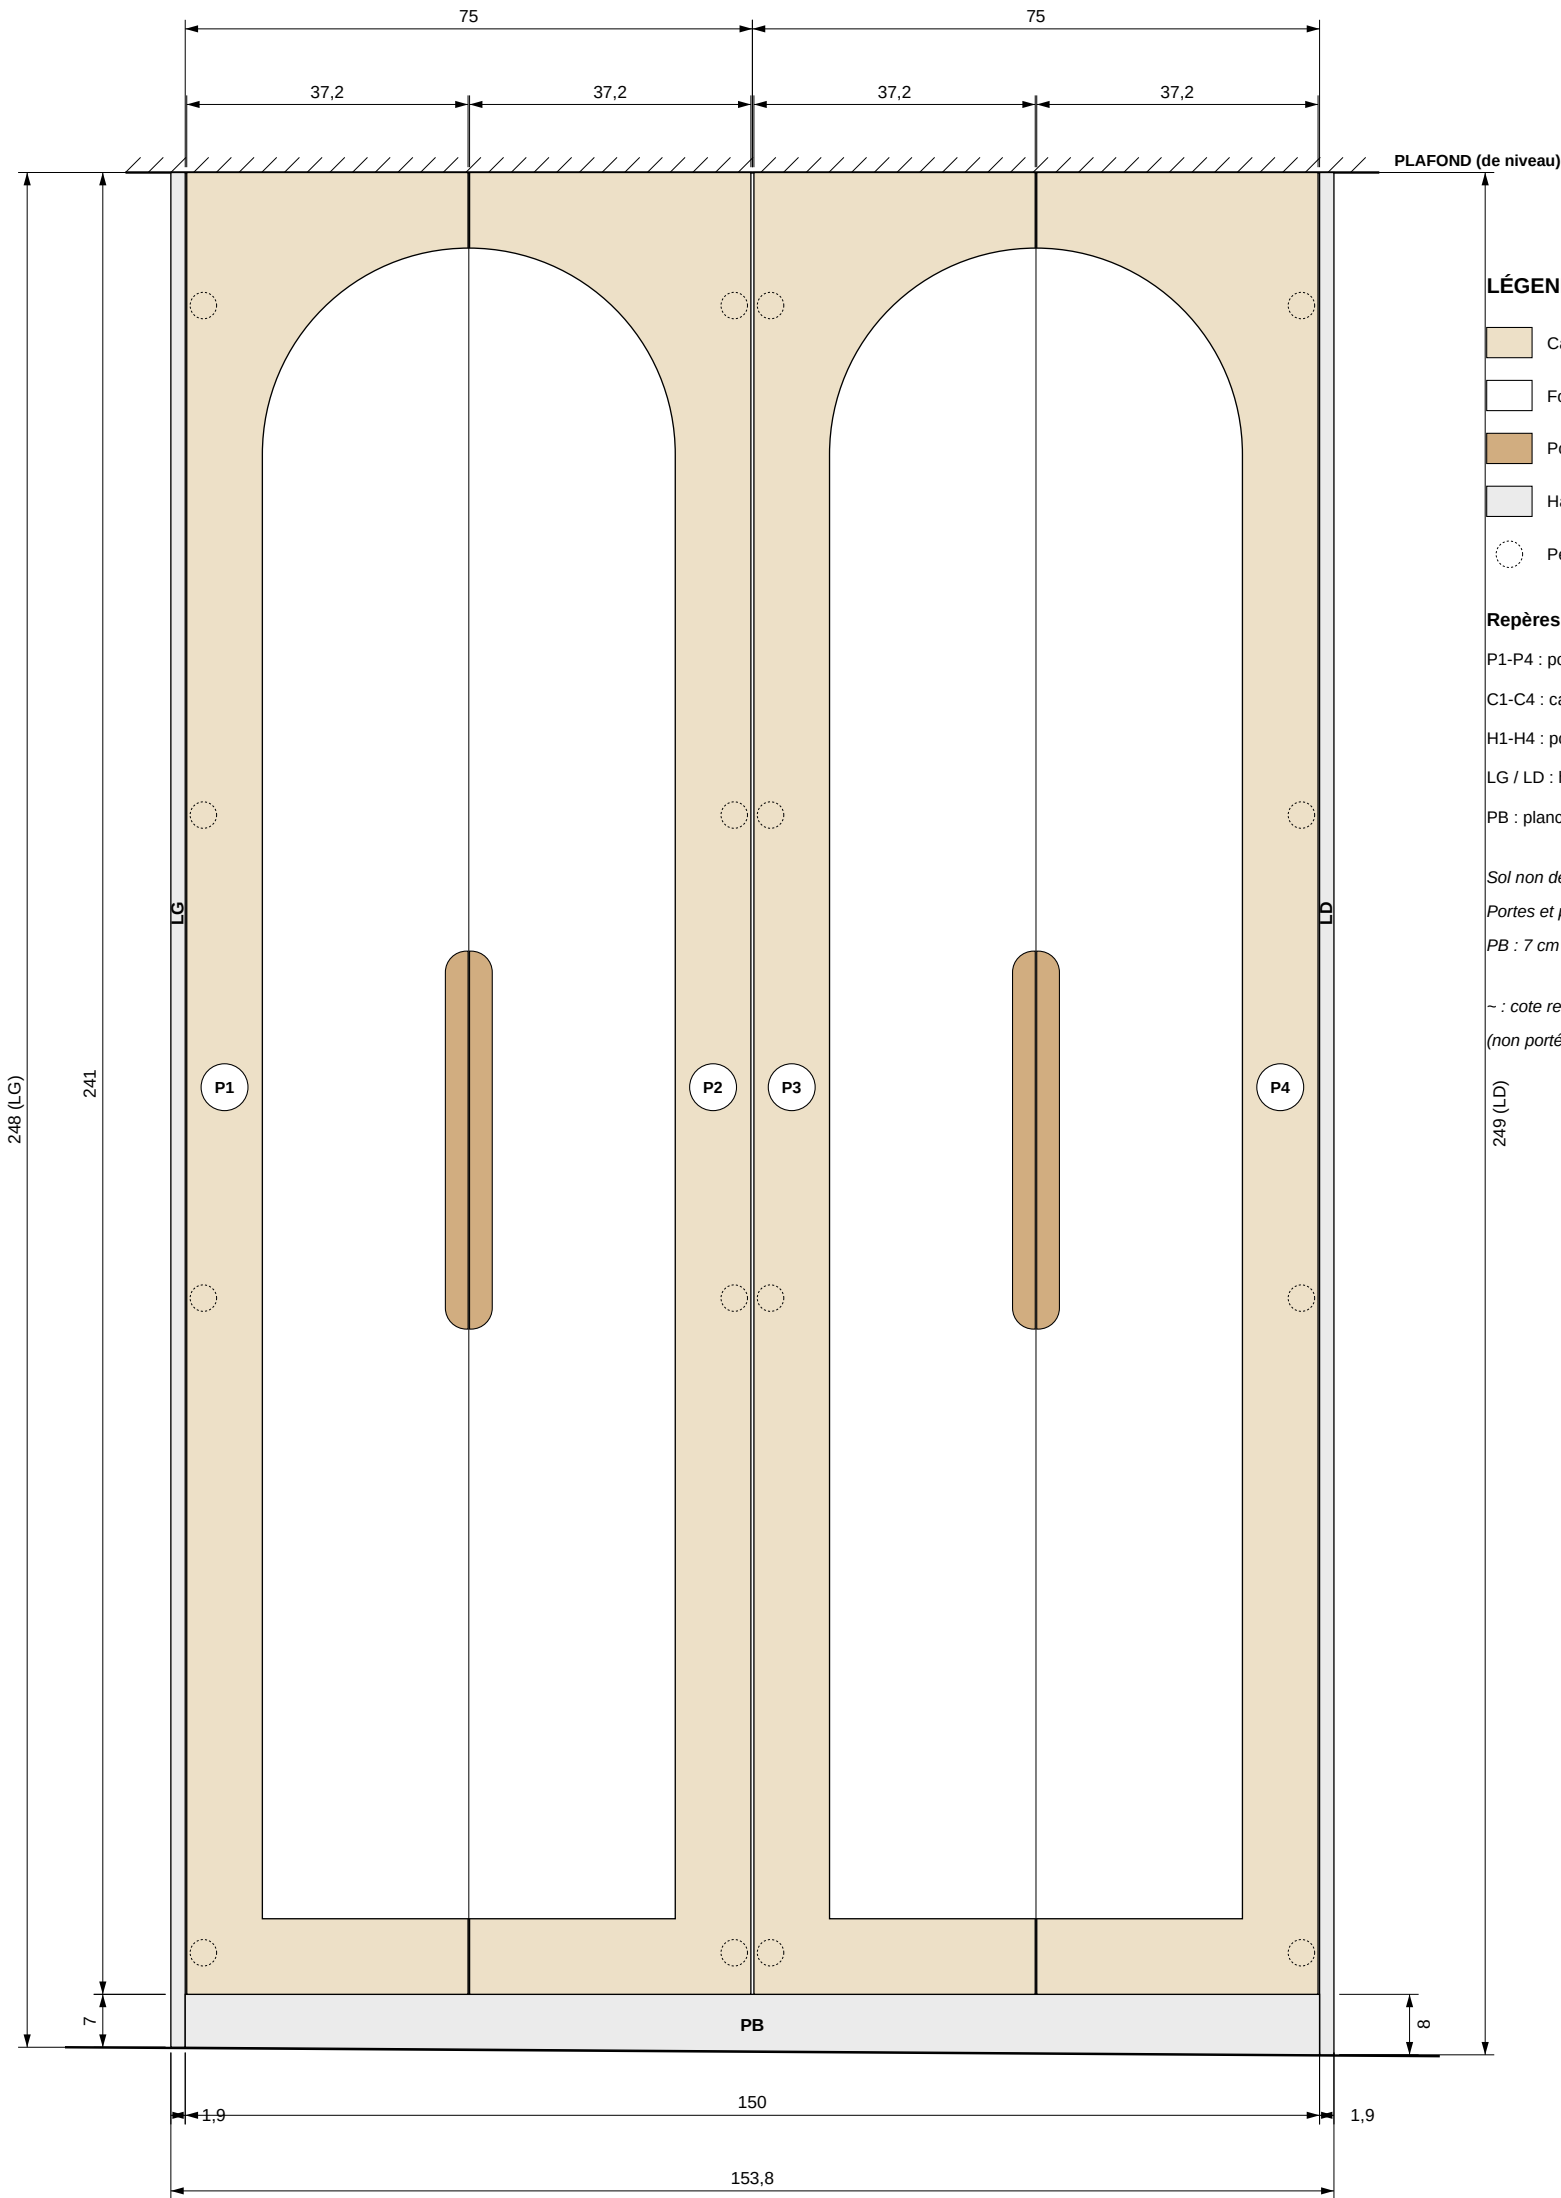

LÉGENDE

- Cadre MDF 5 mm collé sur la porte
- Fond d'alcôve = face de la porte MDF 19
- Poignée bois massif (H)
- Habillages LG/LD (MDF 19), planche PB (MDF 16)
- Perçage charnière Ø35 (face arrière)

Repères


P1-P4 : portes MDF 19
C1-C4 : cadres MDF 5 mm (p. 2)
H1-H4 : poignées (p. 3)
LG / LD : habillages gauche / droit
PB : planche du bas

Sol non de niveau : le bas droit est plus bas.
Portes et plafond de niveau.
PB : 7 cm à gauche, 8 cm à droite.

~ : cote relevée sur le dessin
(non portée sur le plan d'origine)

COUPE HORIZONTALE - vue de dessus (schéma)

Échelle 1:10 - mur du fond hors d'équerre : habillage gauche limité à 10 cm en façade

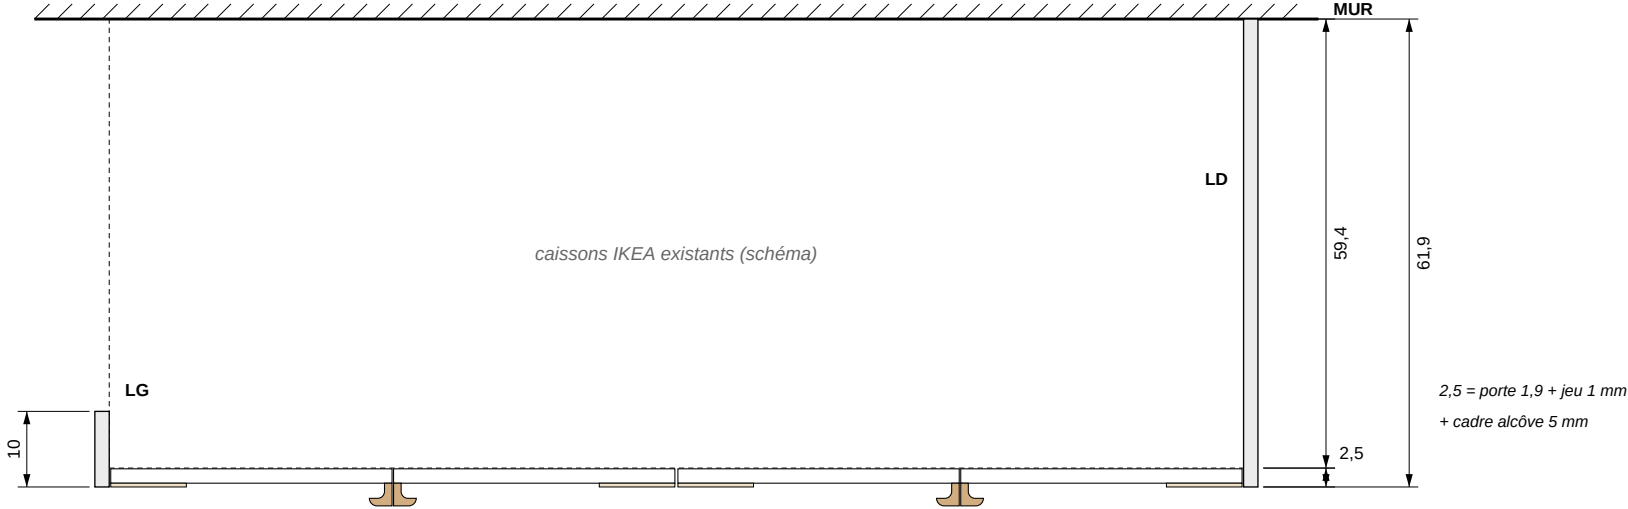

Face avant (cadres 5 mm)

HABILLAGE DRESSING - PORTES À CHARNIÈRES

Vue d'ensemble - vue de face et coupe horizontale

Cotes en cm sauf mention

Échelle indiquée sous chaque vue

Date

28/09/2026

Page

1 / 4

4 charnières par porte (16 au total), cuvette Ø35, porte en applique.
Hauteurs depuis le bas de porte : 5,5 - 92,1 - 156 - 223,4.
P1 et P3 : perçages sur le chant gauche. P2 et P4 : chant droit.
Distance axe de cuvette / chant : non cotée (dessin ~28 mm) -
à fixer selon le modèle de charnière (souvent 21,5 à 23 mm).

Diagram illustrating a quarter-circle fillet (R 27,2) on a rectangular plate. The fillet is defined by a radius of 27,2. The distance from the center of the fillet to the edges of the plate is 10. The fillet is labeled "R 27,2" and "coupe". The center of the fillet is labeled "C1". The fillet is defined by the intersection of two circles of radius 10, centered at (0, 10) and (10, 0) in a coordinate system where the bottom-left corner is the origin. The fillet is the region where the two circles overlap, within the square [0, 10] x [0, 10].

Diagramme technique d'une coupe transversale d'une porte et d'un cadre. La porte a une hauteur de 19 cm. Le cadre a une épaisseur de 5 mm et une largeur de 10 cm. Le creux du cadre a une profondeur de 5 mm.

Porte MDF 19 + cadre MDF 5 mm collé (épaisseur totale 24 mm)

Coupe à hauteur d'alcôve, côté joint : le cadre s'arrête à 10 cm du chant.

Même contour que la porte : 241 x 37,2 cm, ép. 5 mm.

Découpe de l'arche : 27,2 cm de large depuis le chant du joint, haut à 10 cm du haut de la porte, bas à 10 cm du bas de la porte, ouverte sur le chant du joint (voir détail A).

C1/C3 : forme gauche - C2/C4 : forme symétrique (droite).

Cotes de l'alcôve (marge 10 cm côté charnières, largeur 54,4 cm sur deux portes) : déduites du dessin - à valider.


Technical drawing of a door with dimensions and labels. The drawing shows a door with a central opening and a handle. The overall dimensions are 223,4 (width) and 241 (height). The central opening has a width of 54,4 and a height of 156. The handle is a vertical oval shape with a width of 10 and a height of 92,1. The door is divided into two main sections by a vertical line. The left section is labeled 'P1' and the right section is labeled 'P2'. The handle is labeled 'R 27,2'. The drawing includes various dimension lines and labels for specific parts and measurements.

Dimensions and labels:

- Overall width: 223,4
- Overall height: 241
- Top width segments: 37,2 (left), 37,2 (right)
- Top width total: 75
- Top height segment: 10
- Central opening width: 54,4
- Central opening height: 156
- Handle width: 10
- Handle height: 92,1
- Handle radius: R 27,2
- Bottom width segments: 37,2 (left), 37,2 (right)
- Bottom width total: 75
- Bottom height segments: 10 (left), 10 (right)
- Bottom height total: 221
- Labels: P1, P2, R 27,2
- Text: Perçages (depuis le bas de porte)

LG - HABILLAGE GAUCHE


Échelle 1:10 - 1 pièce - MDF 19

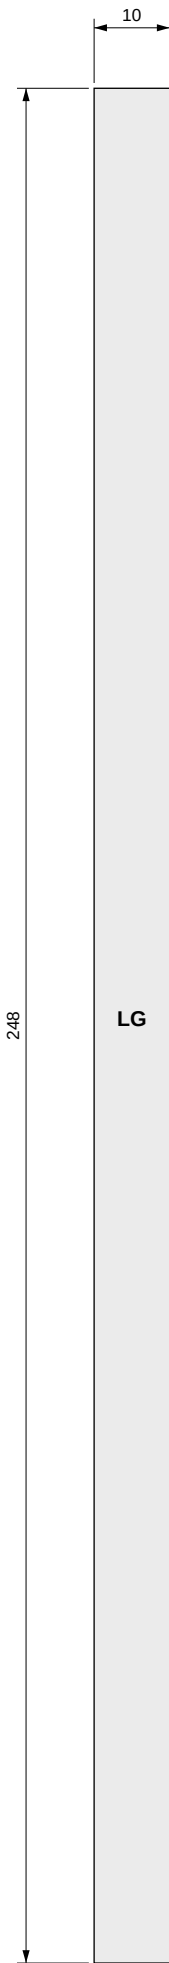

Profondeur 10 cm côté façade seulement (mur hors d'équerre).
Dessus de niveau (plafond), bas posé sur le sol.

LD - HABILLAGE DROIT


Échelle 1:10 - 1 pièce - MDF 19

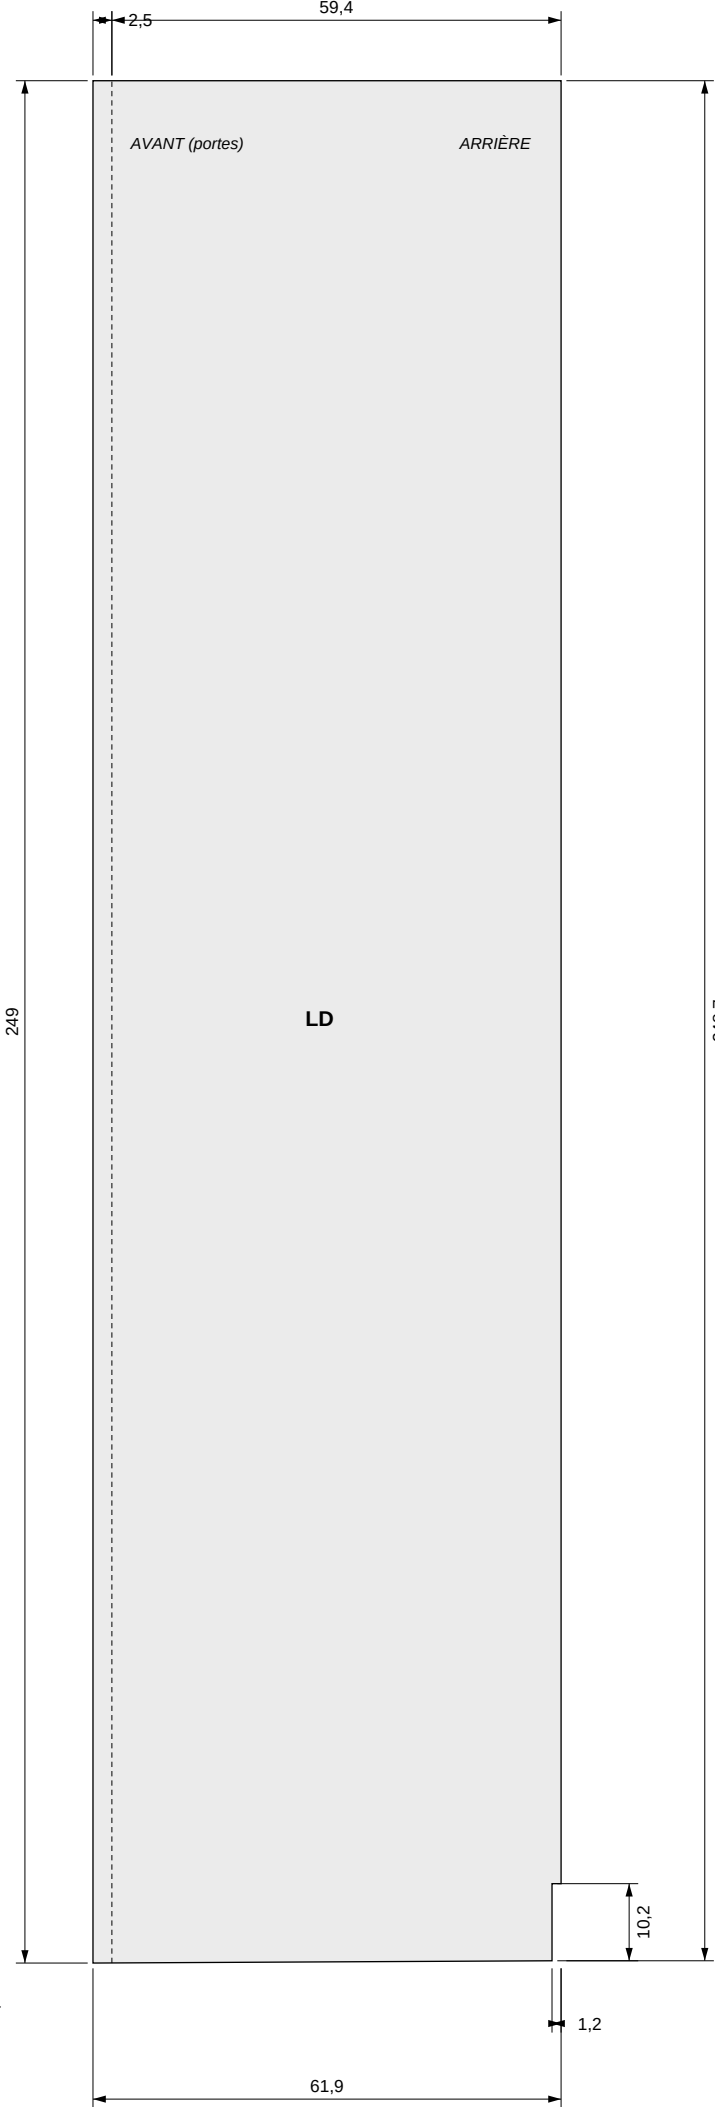

Encoche arrière 10,2 x 1,2 cm en partant du bas, pour la plinthe murale.
Dessus de niveau (plafond) ; bas suivant le sol : 249 devant, 248,7 derrière (sol plus bas à droite).
2,5 = porte 1,9 + jeu 1 mm + cadre d'alcôve 5 mm : l'habillage affleure la face des cadres.

PB - PLANCHE DU BAS


Échelle 1:10 - 1 pièce - MDF 16

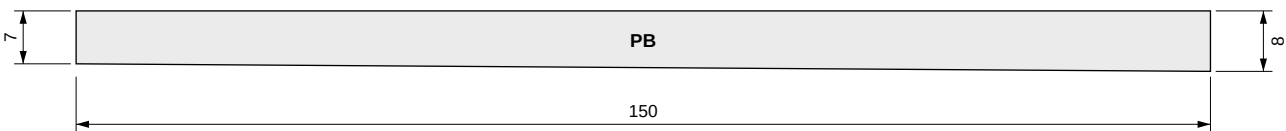

Dessus de niveau (sous les portes) ; bas suivant le sol : 7 cm à gauche, 8 cm à droite.


H1-H4 - POIGNÉES BOIS MASSIF

4 pièces : H1 / H3 (porte gauche), H2 / H4 en miroir. Arrondi côté extérieur.

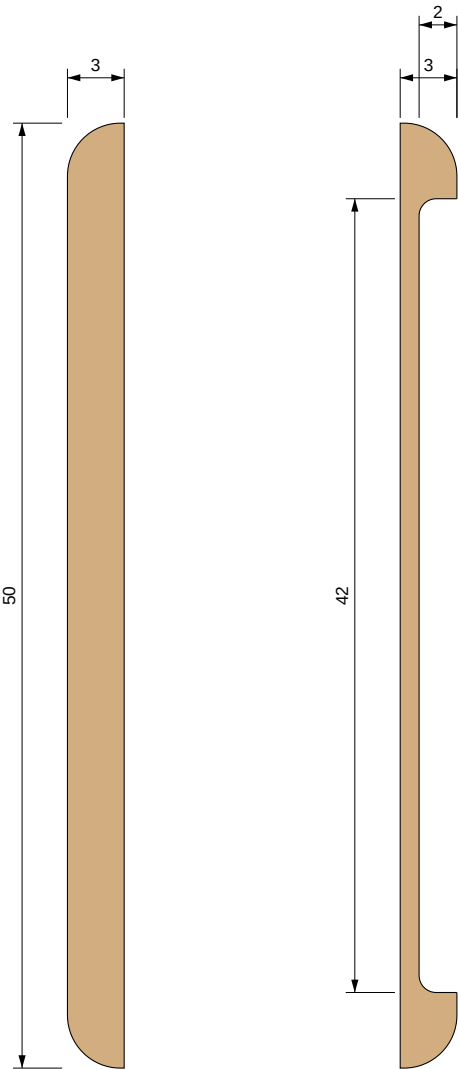

Vue de face
pleine - 1:4

Vue de derrière
évidement 42 x 2 - 1:4

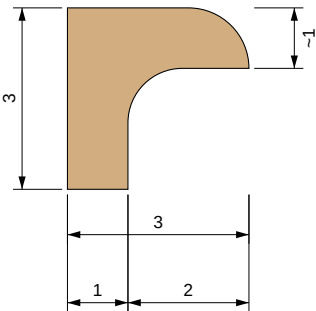

Coupe (échelle 1:1,25)

plaque en façade
patte de fixation côté joint
(1 cm supposé)
évidement (doigts)

À confirmer avec le menuisier :
- épaisseur de la plaque de façade (~1 cm supposé)
- profondeur de l'évidement, essence, fixation

TABLEAU DE DÉBIT

Dimensions finies en cm (long. x larg.), épaisseurs en mm. Sens du fil non imposé (MDF).

Repère	Désignation	Qté	Long. (cm)	Larg. (cm)	Ép. (mm)	Matériau	Usinages / remarques
P1, P3	Porte gauche	2	241	37,2	19	MDF 19	4 perçages charnière cuvette Ø35 sur le chant gauche (5,5 / 92,1 / 156 / 223,4 depuis le bas). Alcôve : cadre C collé sur la face.
P2, P4	Porte droite (symétrique)	2	241	37,2	19	MDF 19	Idem P1, perçages sur le chant droit.
C1, C3	Cadre d'alcôve gauche	2	241	37,2	5	MDF 5	Découpe de l'arche (R 27,2), ouverte sur le chant du joint ; marges 10 cm haut / bas / côté charnières. Collé sur P1 / P3.
C2, C4	Cadre d'alcôve droit (symétrique)	2	241	37,2	5	MDF 5	Idem C1, en miroir. Collé sur P2 / P4.
H1 à H4	Poignée	4	50	3	30	Bois massif	Section en équerre 3 x 3 cm (plaque de façade ~10 mm, patte de fixation 10 mm côté joint), évidée au dos sur 42 x 2 cm côté extérieur, angles intérieurs arrondis, extrémités coupées droit côté extérieur. Deux coins extérieurs très arrondis (vue de face). H2 / H4 en miroir. Essence à préciser.
LG	Habillage gauche	1	248	10	19	MDF 19	Profondeur 10 cm côté façade uniquement (mur hors d'équerre).
LD	Habillage droit	1	249 (avant) 248,7 (arrière)	61,9	19	MDF 19	Profondeur 59,4 + 2,5 (porte 1,9 + jeu 1 mm + cadre 5 mm). Encoche arrière 10,2 x 1,2 en partant du bas (plinthe). Dessus de niveau (plafond), bas suivant le sol.
PB	Planche du bas	1	150	7 (gauche) 8 (droite)	16	MDF 16	Trapèze : dessus de niveau sous les portes, bas suivant le sol (plus bas à droite).